




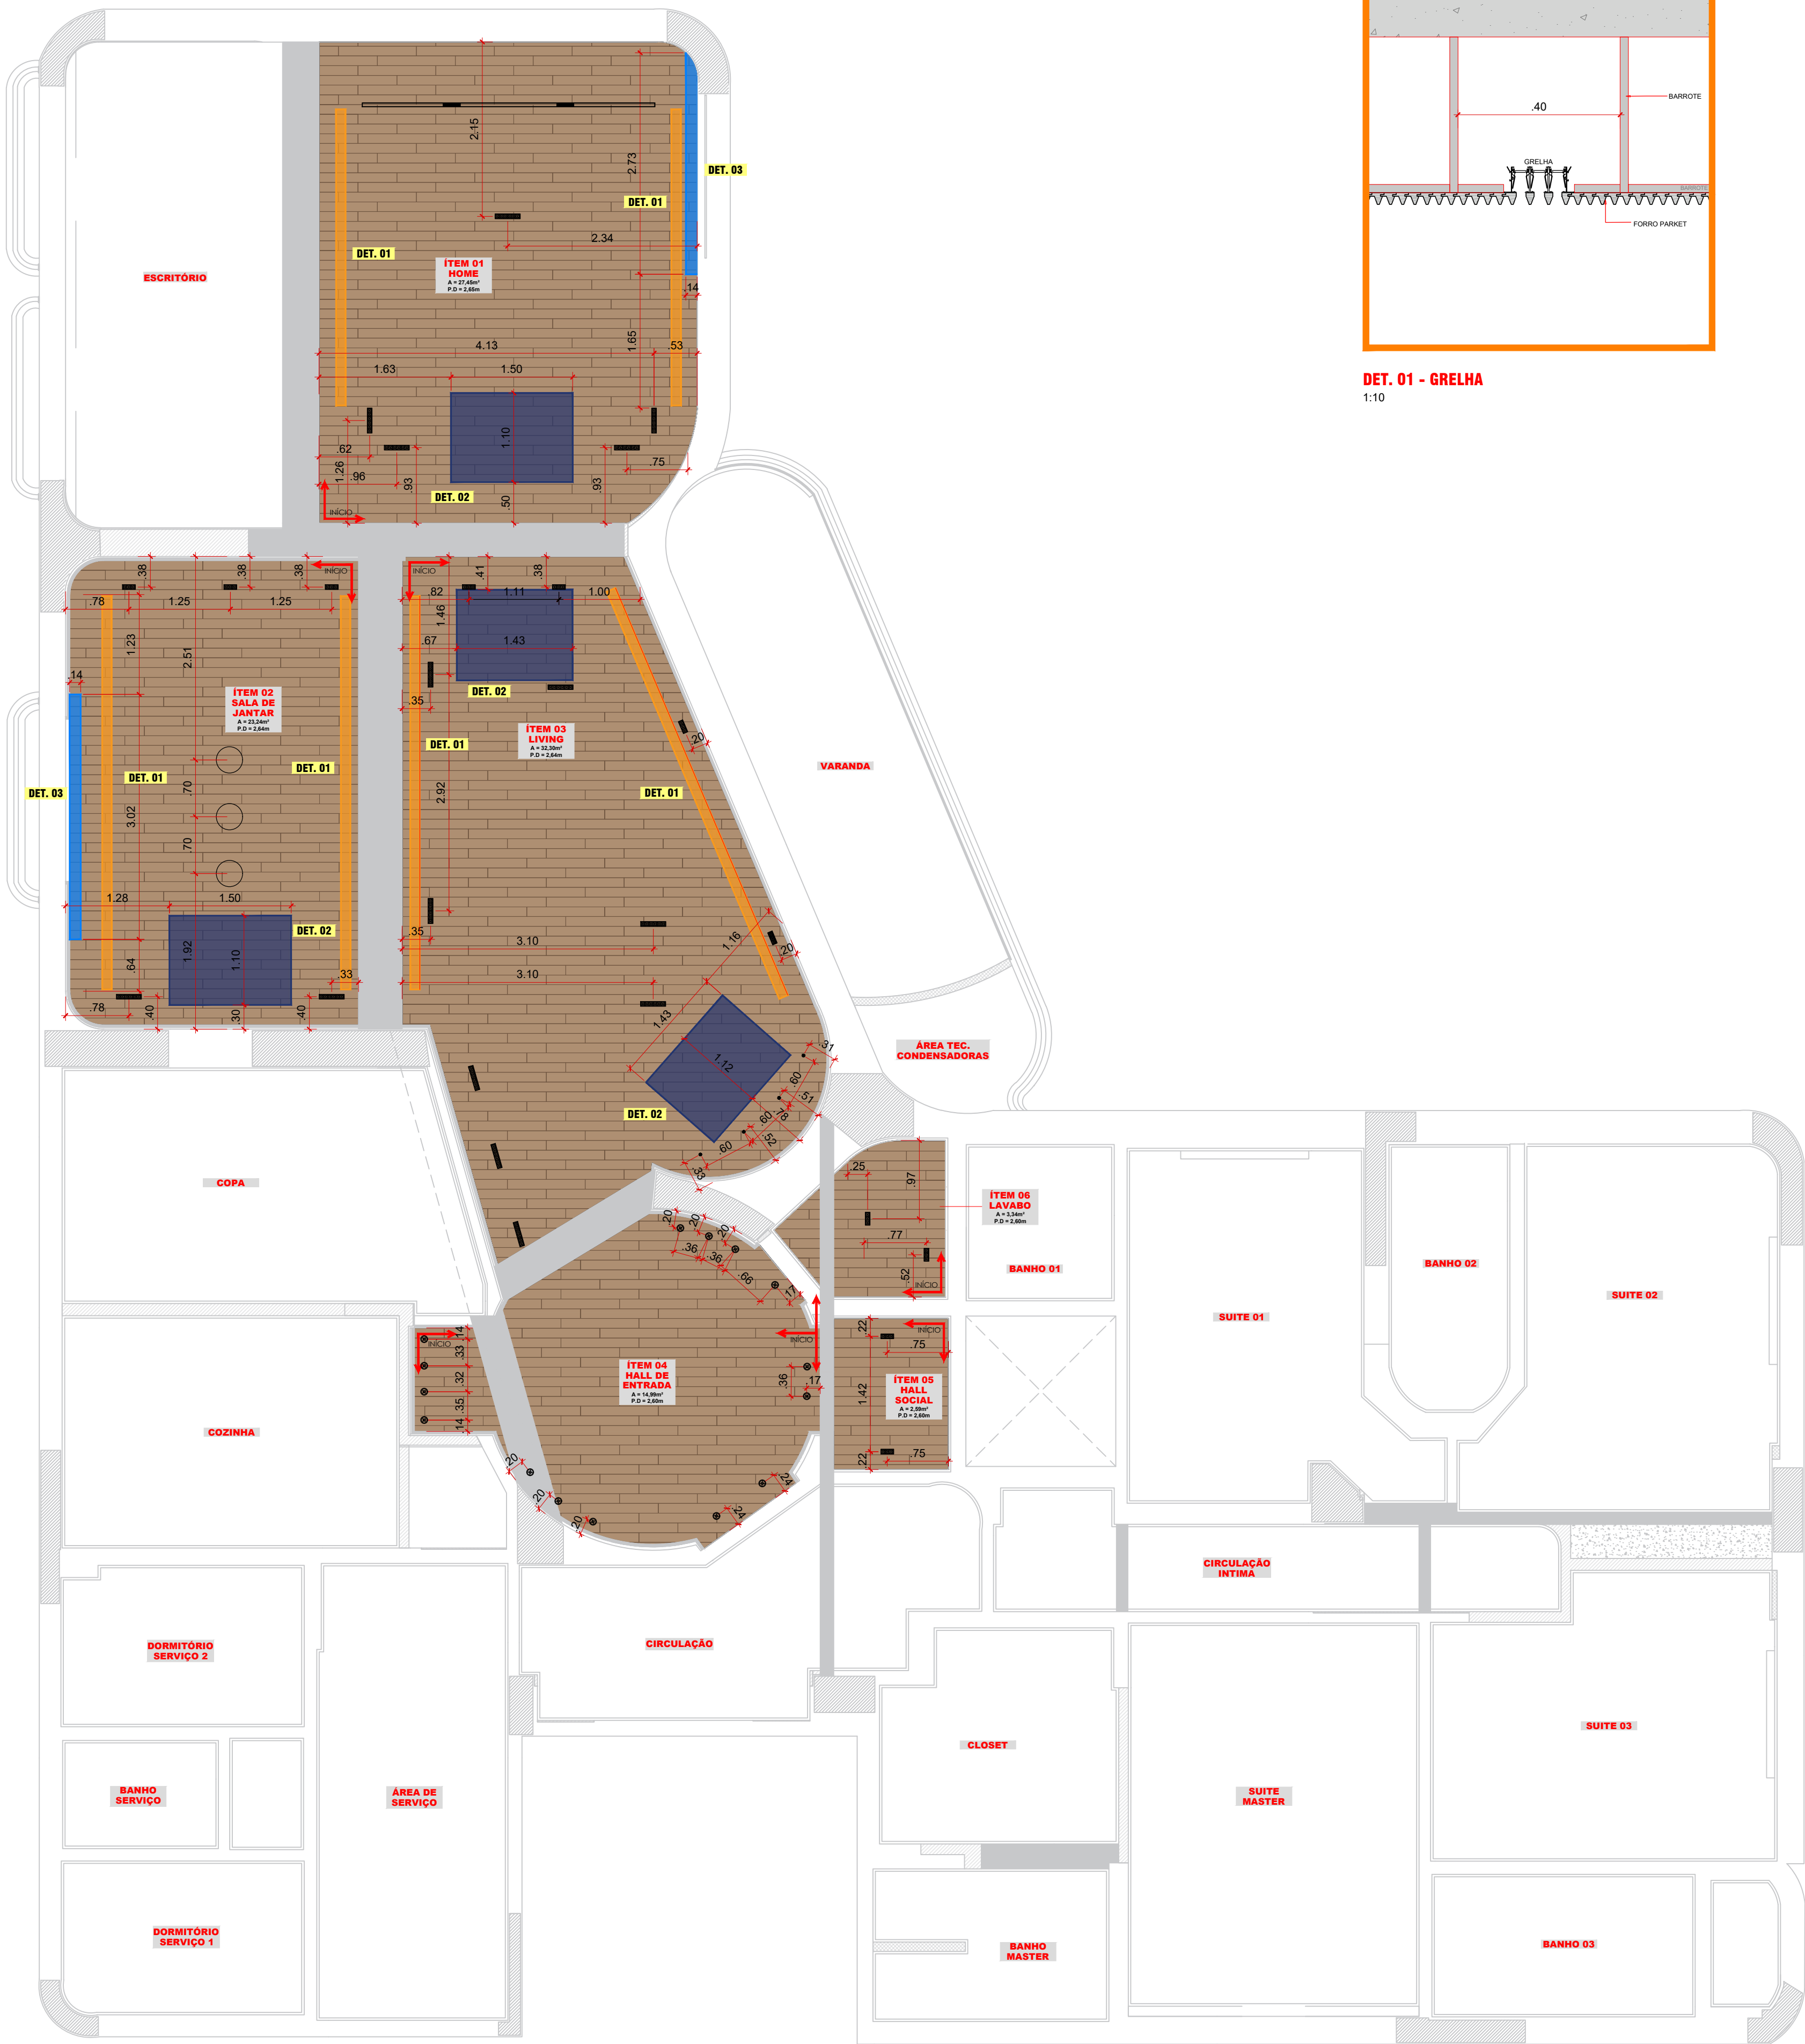


PLANTA DE PAGINAÇÃO DE FORRO
1:50

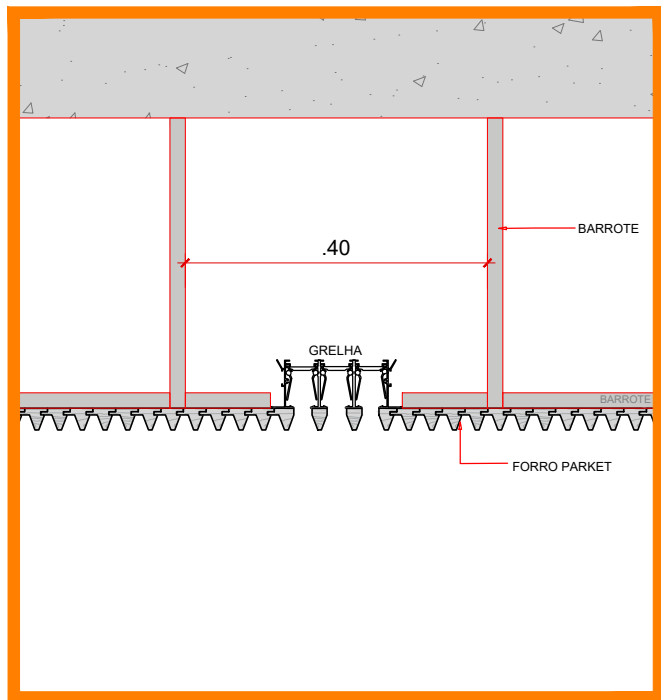

DET. 01 - GRELHA
1:10

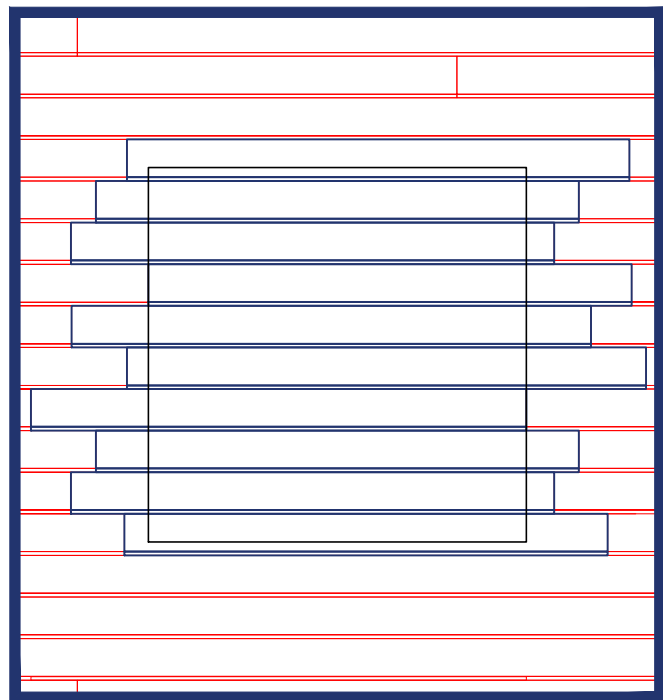

DET. 05 - ALÇAPÃO
1:10

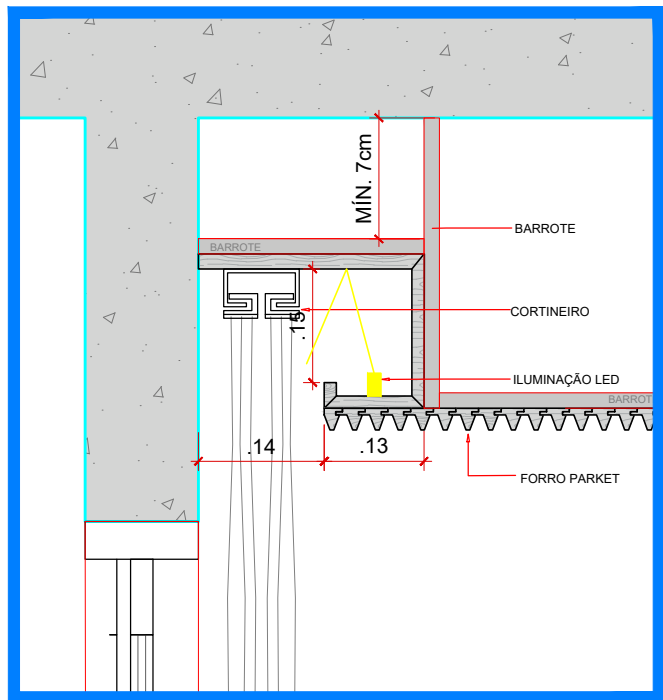

DET. 03 - CORTINEIRO ILUMINADO
1:10

GRELHA - AMBIENTES			
APARTAMENTO	ITEM 01D	HOME	7,32ml
	ITEM 02D	SALA DE JANTAR	9,70ml
	ITEM 03D	LIVING	9,30ml
TOTAL PAVIMENTO			26,23ml
TOTAL OBRA			26,23ml

ALÇAPÃO - AMBIENTES			
APARTAMENTO	ITEM 01C	HOME	1 un.
	ITEM 02C	SALA DE JANTAR	1 un.
	ITEM 03C	LIVING	2 un.
TOTAL PAVIMENTO			4 un.
TOTAL OBRA			4 un.

RECORTES - AMBIENTES			
APARTAMENTO	ITEM 01B	HOME	5 un.
	ITEM 02B	SALA DE JANTAR	6 un.
	ITEM 03B	LIVING	19 un.
	ITEM 04B	HALL DE ENTRADA	15 un.
	ITEM 05B	HALL SOCIAL	2 un.
	ITEM 06B	LAVABO	2 un.
TOTAL PAVIMENTO			49 un.
TOTAL OBRA			49 un.

CORTINEIRO - AMBIENTES			
APARTAMENTO	ITEM 01A	HOME	2,73ml
	ITEM 02A	SALA DE JANTAR	3,02ml
TOTAL PAVIMENTO			5,75ml
TOTAL OBRA			5,75ml

FORRO - AMBIENTES			
APARTAMENTO	ITEM 01	HOME	27,45m²
	ITEM 02	SALA DE JANTAR	23,24m²
	ITEM 03	LIVING	32,30m²
	ITEM 04	HALL DE ENTRADA	14,99m²
	ITEM 05	HALL SOCIAL	2,59m²
	ITEM 06	LAVABO	3,24m²
TOTAL PAVIMENTO			103,81m²
TOTAL OBRA			103,81m²

LEGENDA DE ACABAMENTOS			
TIPO DE SERVIÇO:			
FIXADO NA LAJE COM BARROTES NO EIXO DE 40 A 40CM			
DESCRIÇÃO DE MATERIAL:			
RIPADO TAUARI PREMIUM TG 1,8'3,5+0,5CM BUNHA PROF. BIT 0,8CM - COMP. 90A360CM			

DATA	REV.	DESCRIÇÃO	PROJETISTA
23/04/2026	00	EXECUTIVO INICIAL	VINIcius SANTOS

PARKET

PAGINAÇÃO DE FORRO

FOLHA 01.01

MATHEUS DE ABREU COSTANTINI			
2453	RUA CAÇONDE, 471- 4. A JARDIM PAULISTA SAO PAULO-SP	ANDRACI ATIQUE ABRIL/2026	1:50