




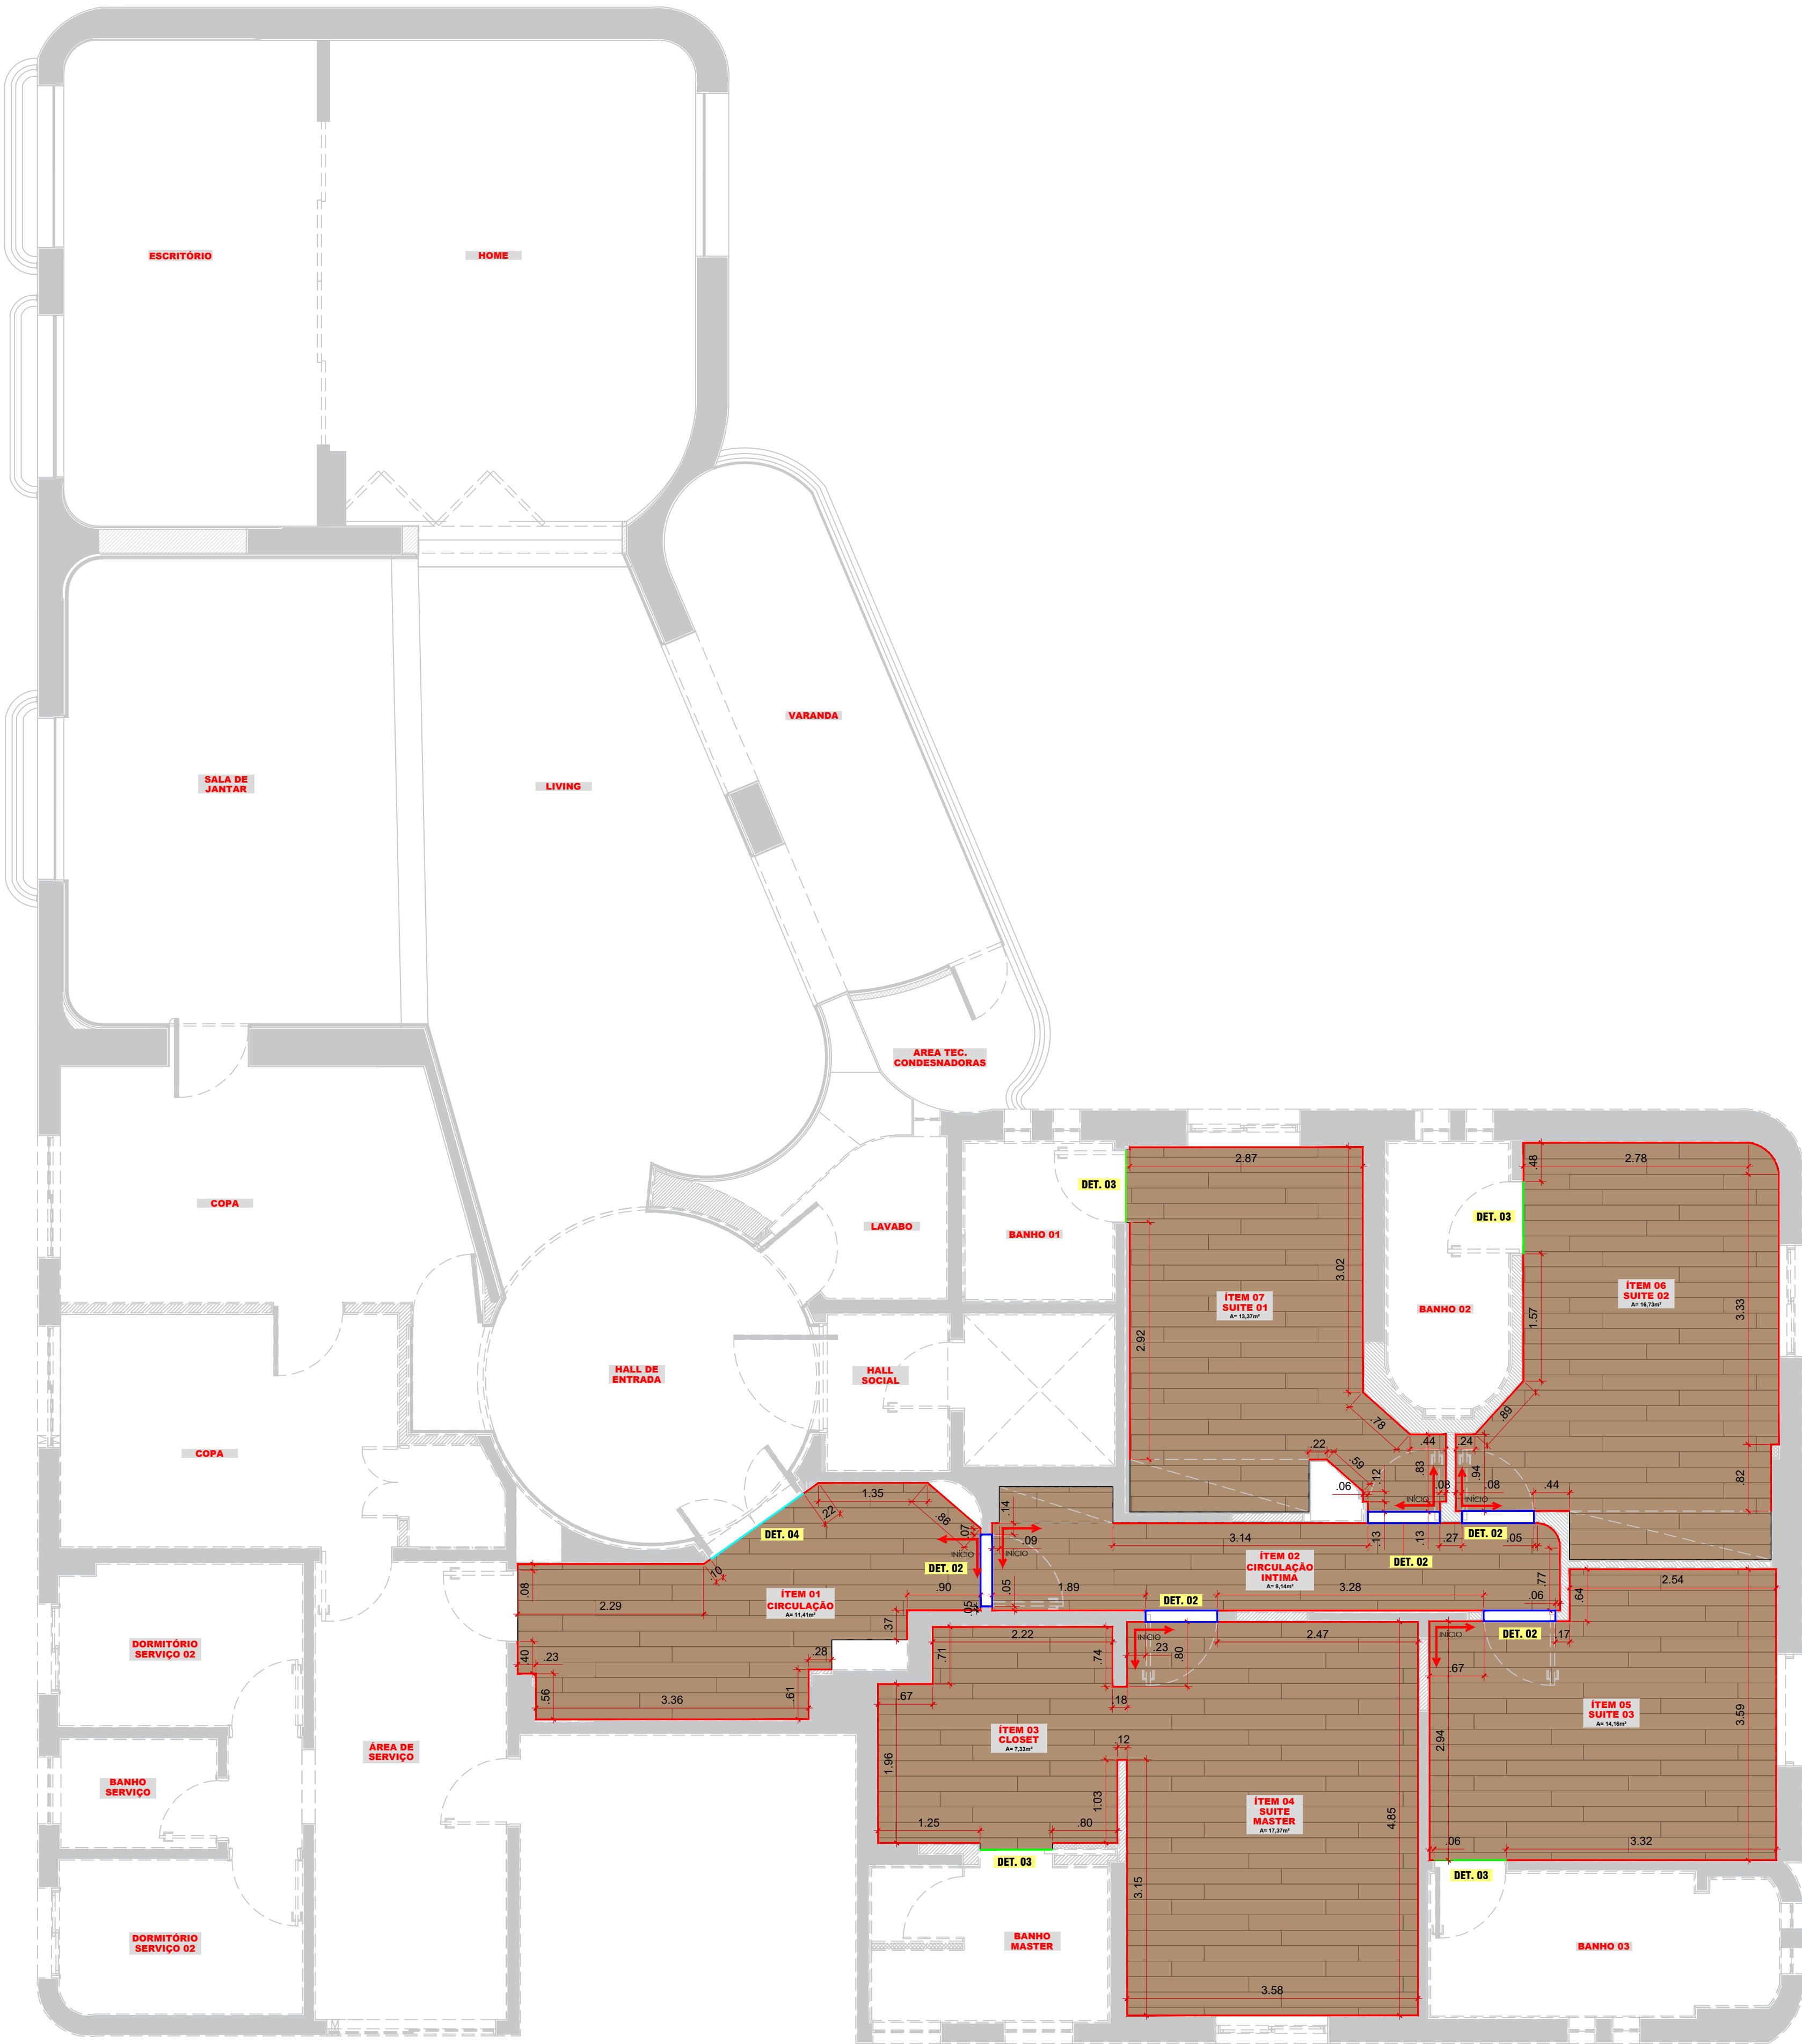


PLANTA DE PAGINAÇÃO DE PISO
1:50

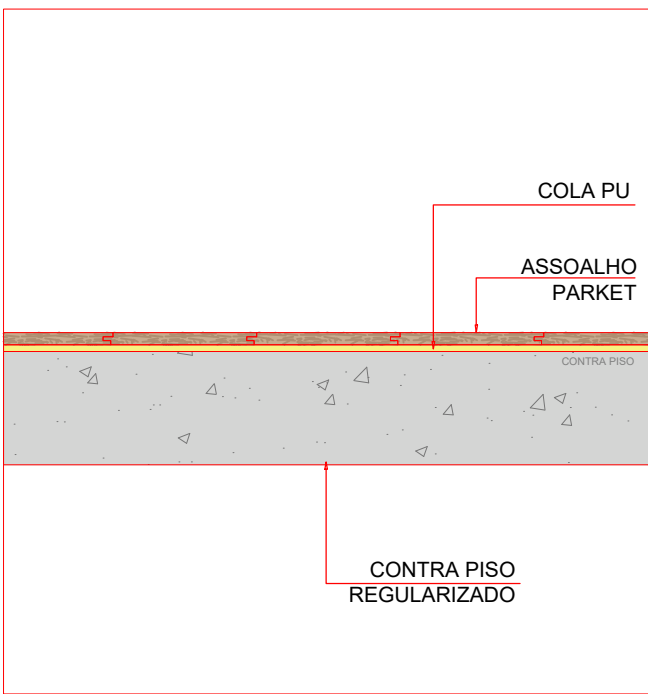


DET. FIXAÇÃO DE ASSOALHO
1:10

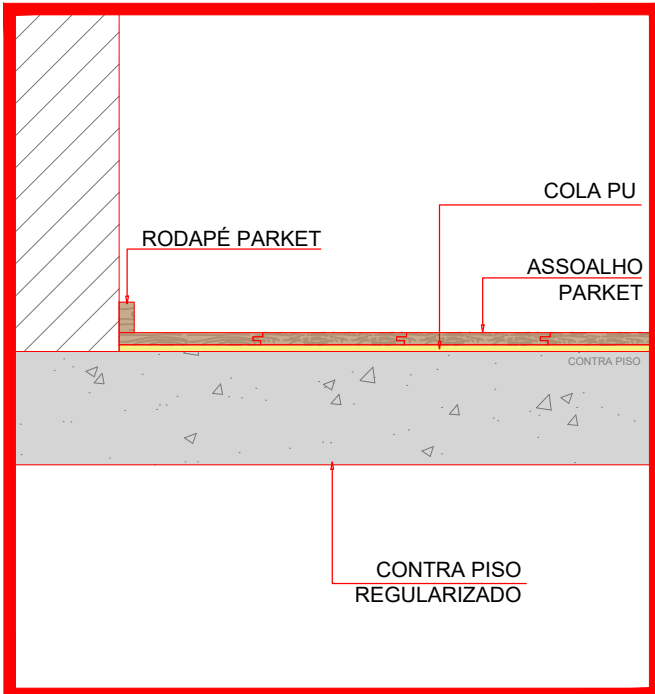


DET. 01 - RODAPÉ
1:10

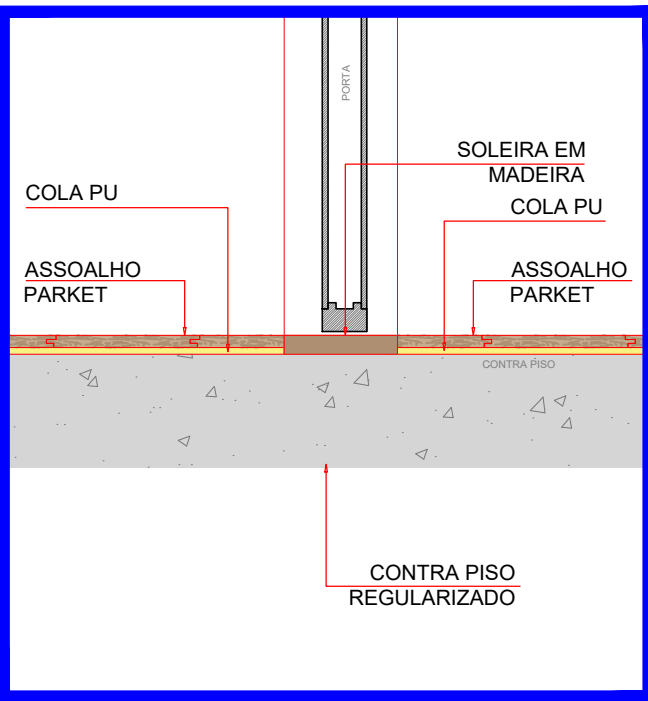

DET. 02 - TRANSIÇÃO DE PISO
1:10

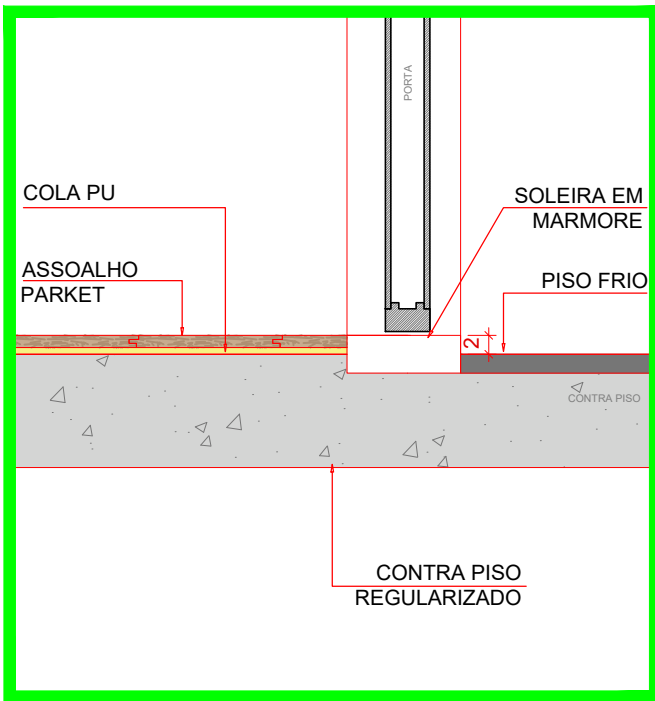

DET. 03 - TRANSIÇÃO DE PISO
1:10

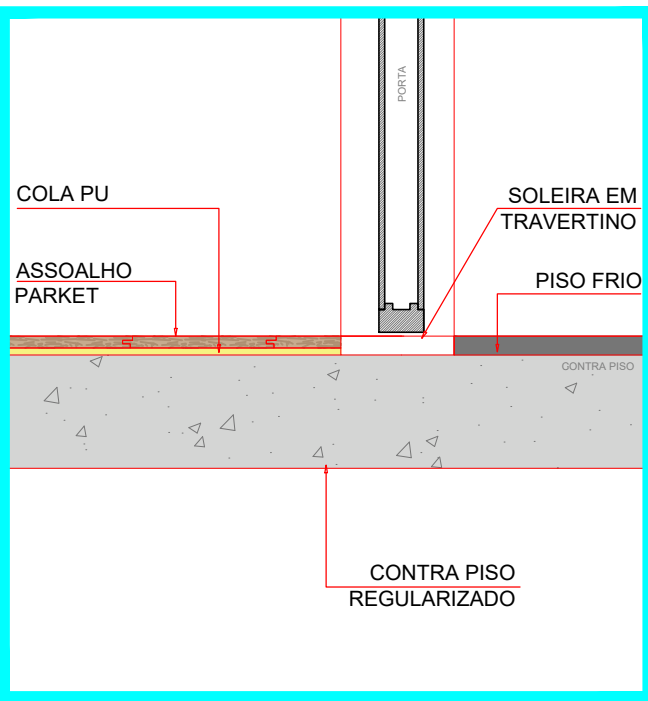

DET. 04 - TRANSIÇÃO DE PISO
1:10

RODAPÉS - AMBIENTES			
PAVIMENTO	ÍTEM 01A	CIRCULAÇÃO	11,73ml
	ÍTEM 02A	CIRCULAÇÃO INTIMA	10,17ml
	ÍTEM 03A	CLOSET	16,21ml
	ÍTEM 04A	SUITE MASTER	15,08ml
	ÍTEM 05A	SUITE 03	13,93ml
	ÍTEM 06A	SUITE 02	11,57ml
	ÍTEM 07A	SUITE 01	11,41ml
TOTAL PAVIMENTO			90ml
TOTAL OBRA			90ml

PISO - AMBIENTES			
PAVIMENTO	ÍTEM 01	CIRCULAÇÃO	11,41m²
	ÍTEM 02	CIRCULAÇÃO INTIMA	8,14m²
	ÍTEM 03	CLOSET	7,33m²
	ÍTEM 04	SUITE MASTER	17,37m²
	ÍTEM 05	SUITE 03	14,16m²
	ÍTEM 06	SUITE 02	16,73m²
	ÍTEM 07	SUITE 01	13,37m²
TOTAL PAVIMENTO			88,51m²
TOTAL OBRA			88,51m²

LEGENDA DE ACABAMENTOS			
TIPO DE SERVIÇO:			
ASSOALHO COLADO COM COLA PU DIRETAMENTE NO CONTRAPISO			
DESCRIÇÃO DE MATERIAL:			
CARVALHO EUROPEU NATURAL TG 1,5/3 X 19 X 190CM			
DATA	REV.	DESCRIÇÃO	PROJETISTA
23/04/2026	00	EXECUTIVO INICIAL	VINICIUS SANTOS

PARKET

PAGINAÇÃO DE PISO

FOLHA 01.01

MATHEUS DE ABREU COSTANTINI			
2453	RUA CAÇONDE, 471- 4. A JARDIM PAULISTA SAO PAULO-SP	PROJETO ANDRACI ATIQUE ABRIL/2026	1:50